

LV distribution diagram

Transformer-fed distribution and outgoing circuits.

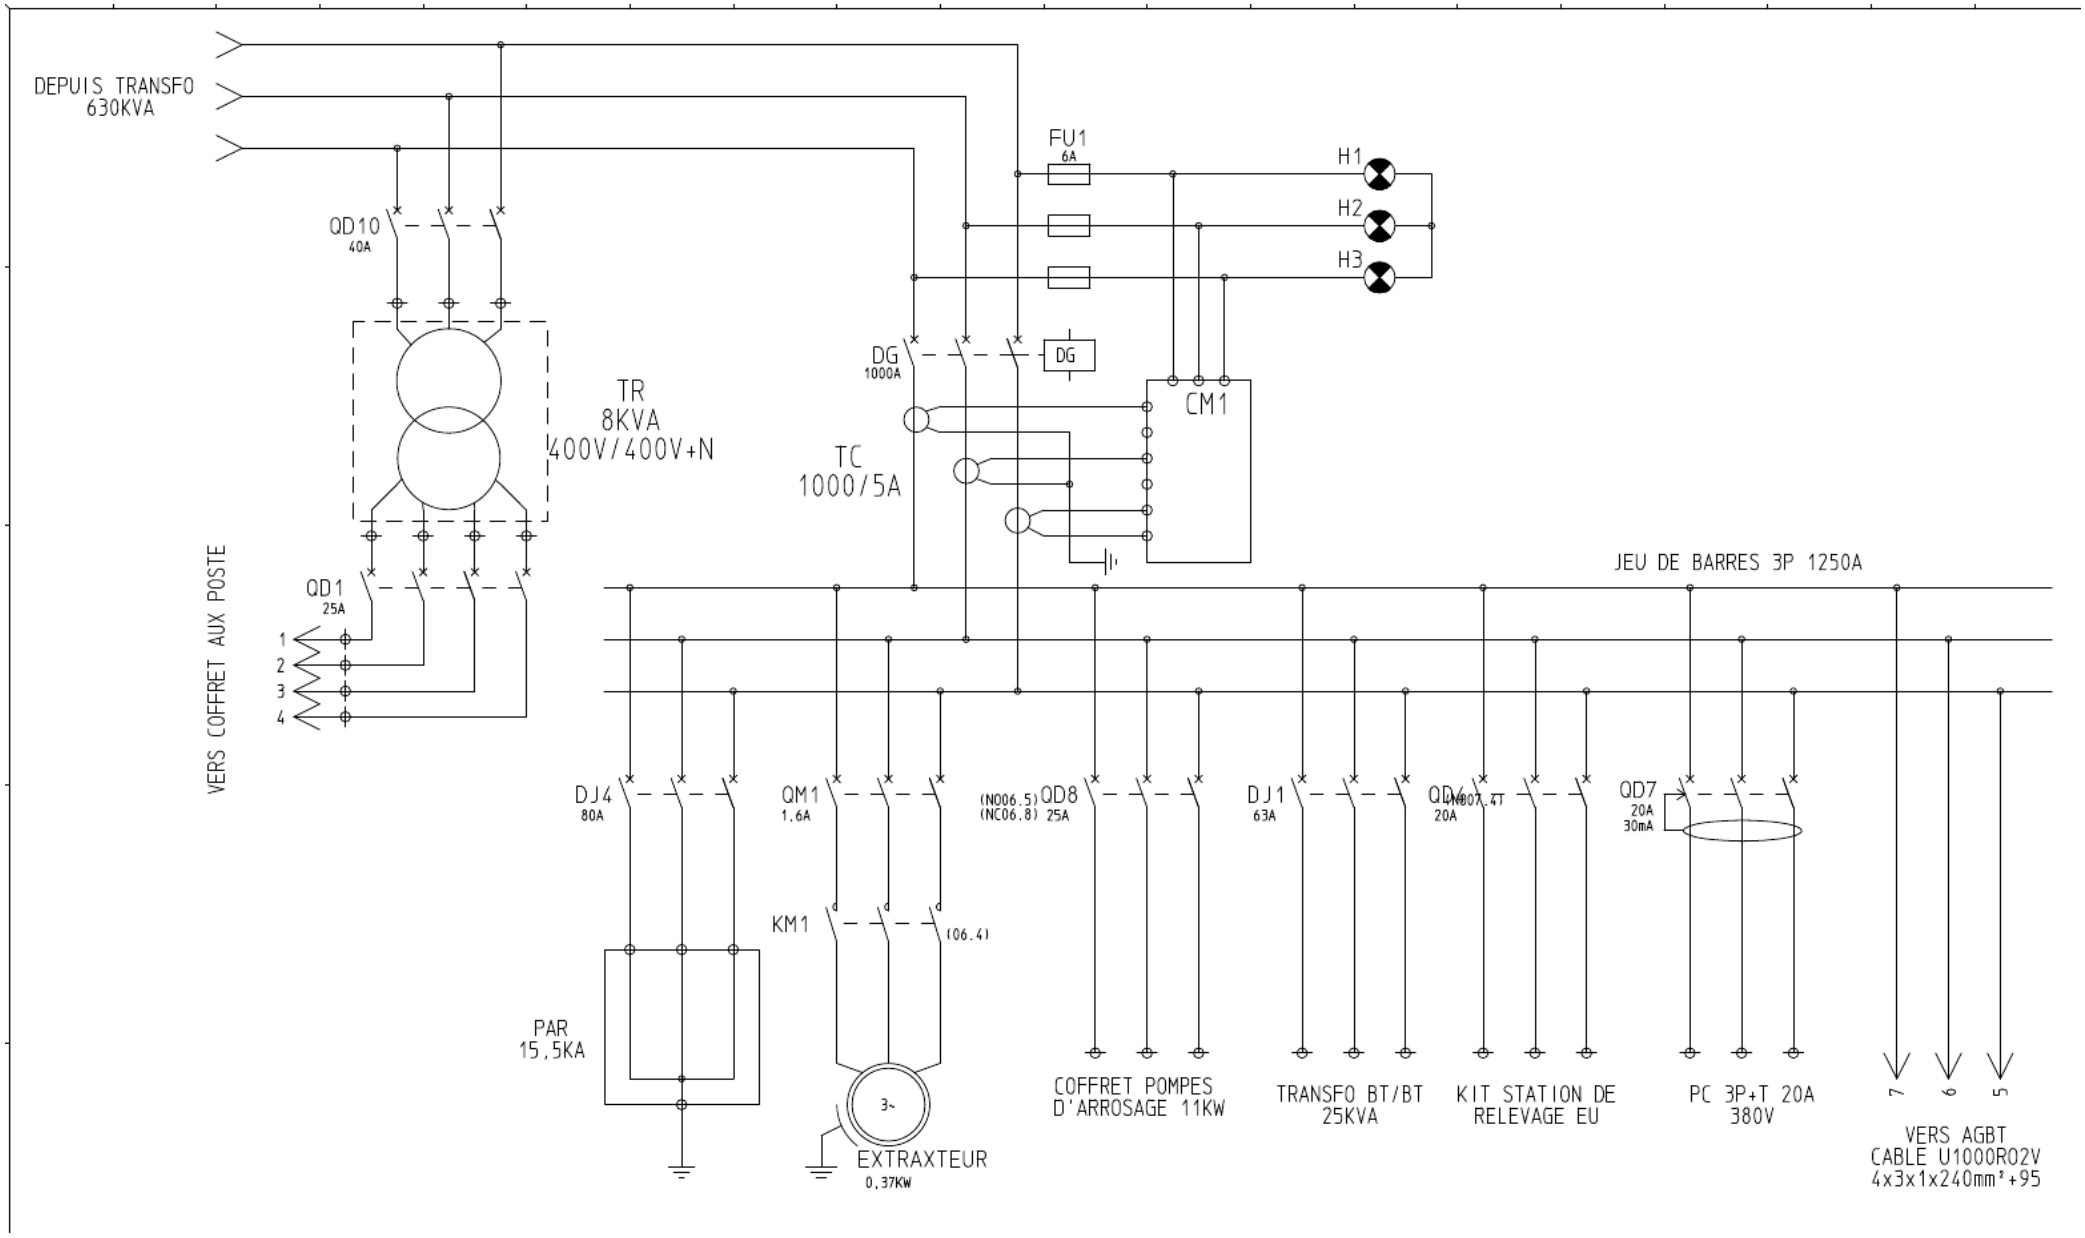


Incoming LV panel

Incoming metering and panel protection.

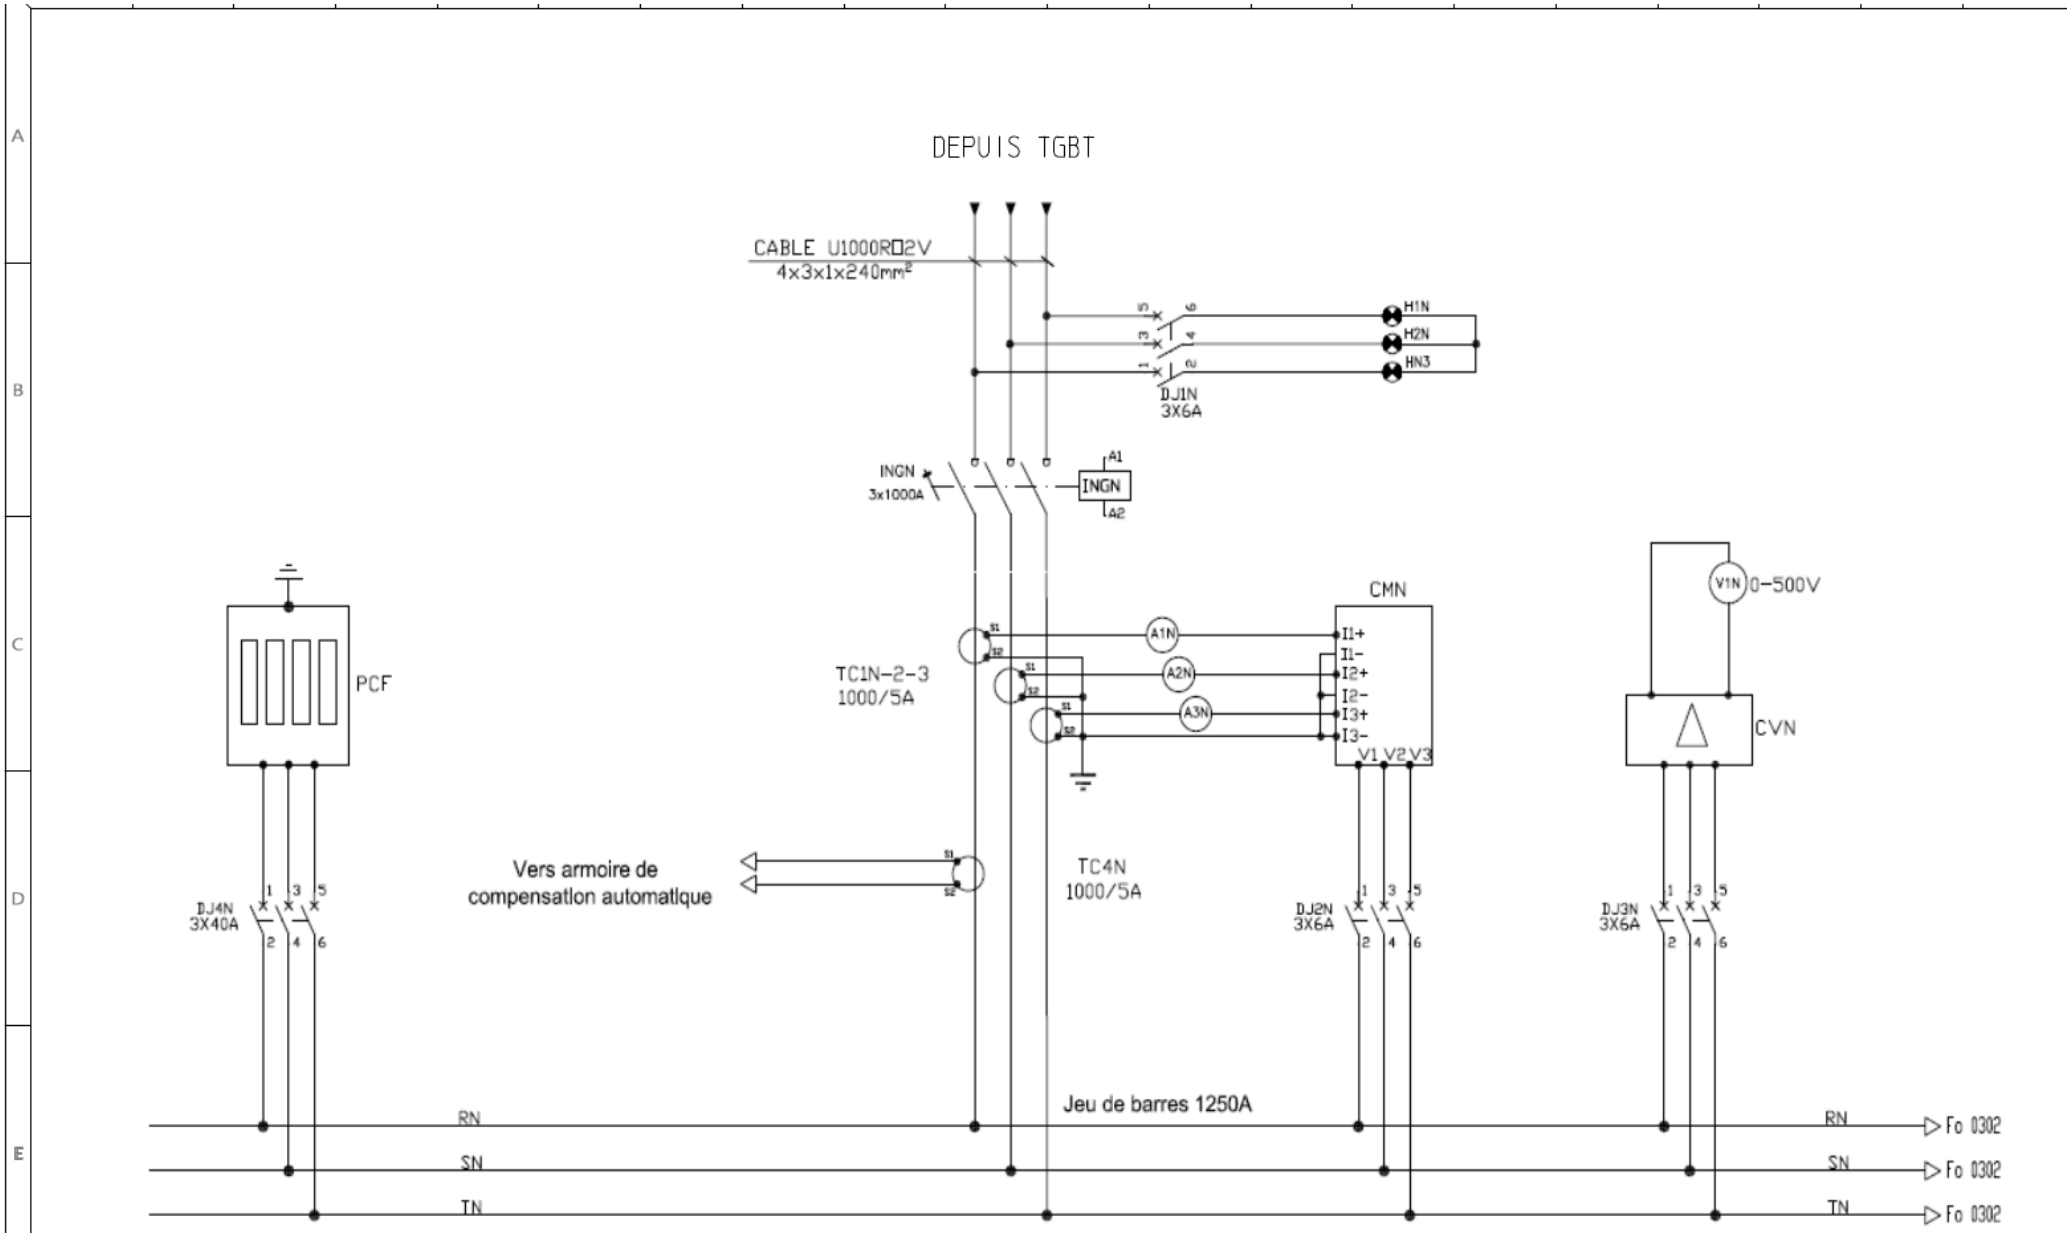


Power-factor compensation

Compensation-bank supply and branch circuits.

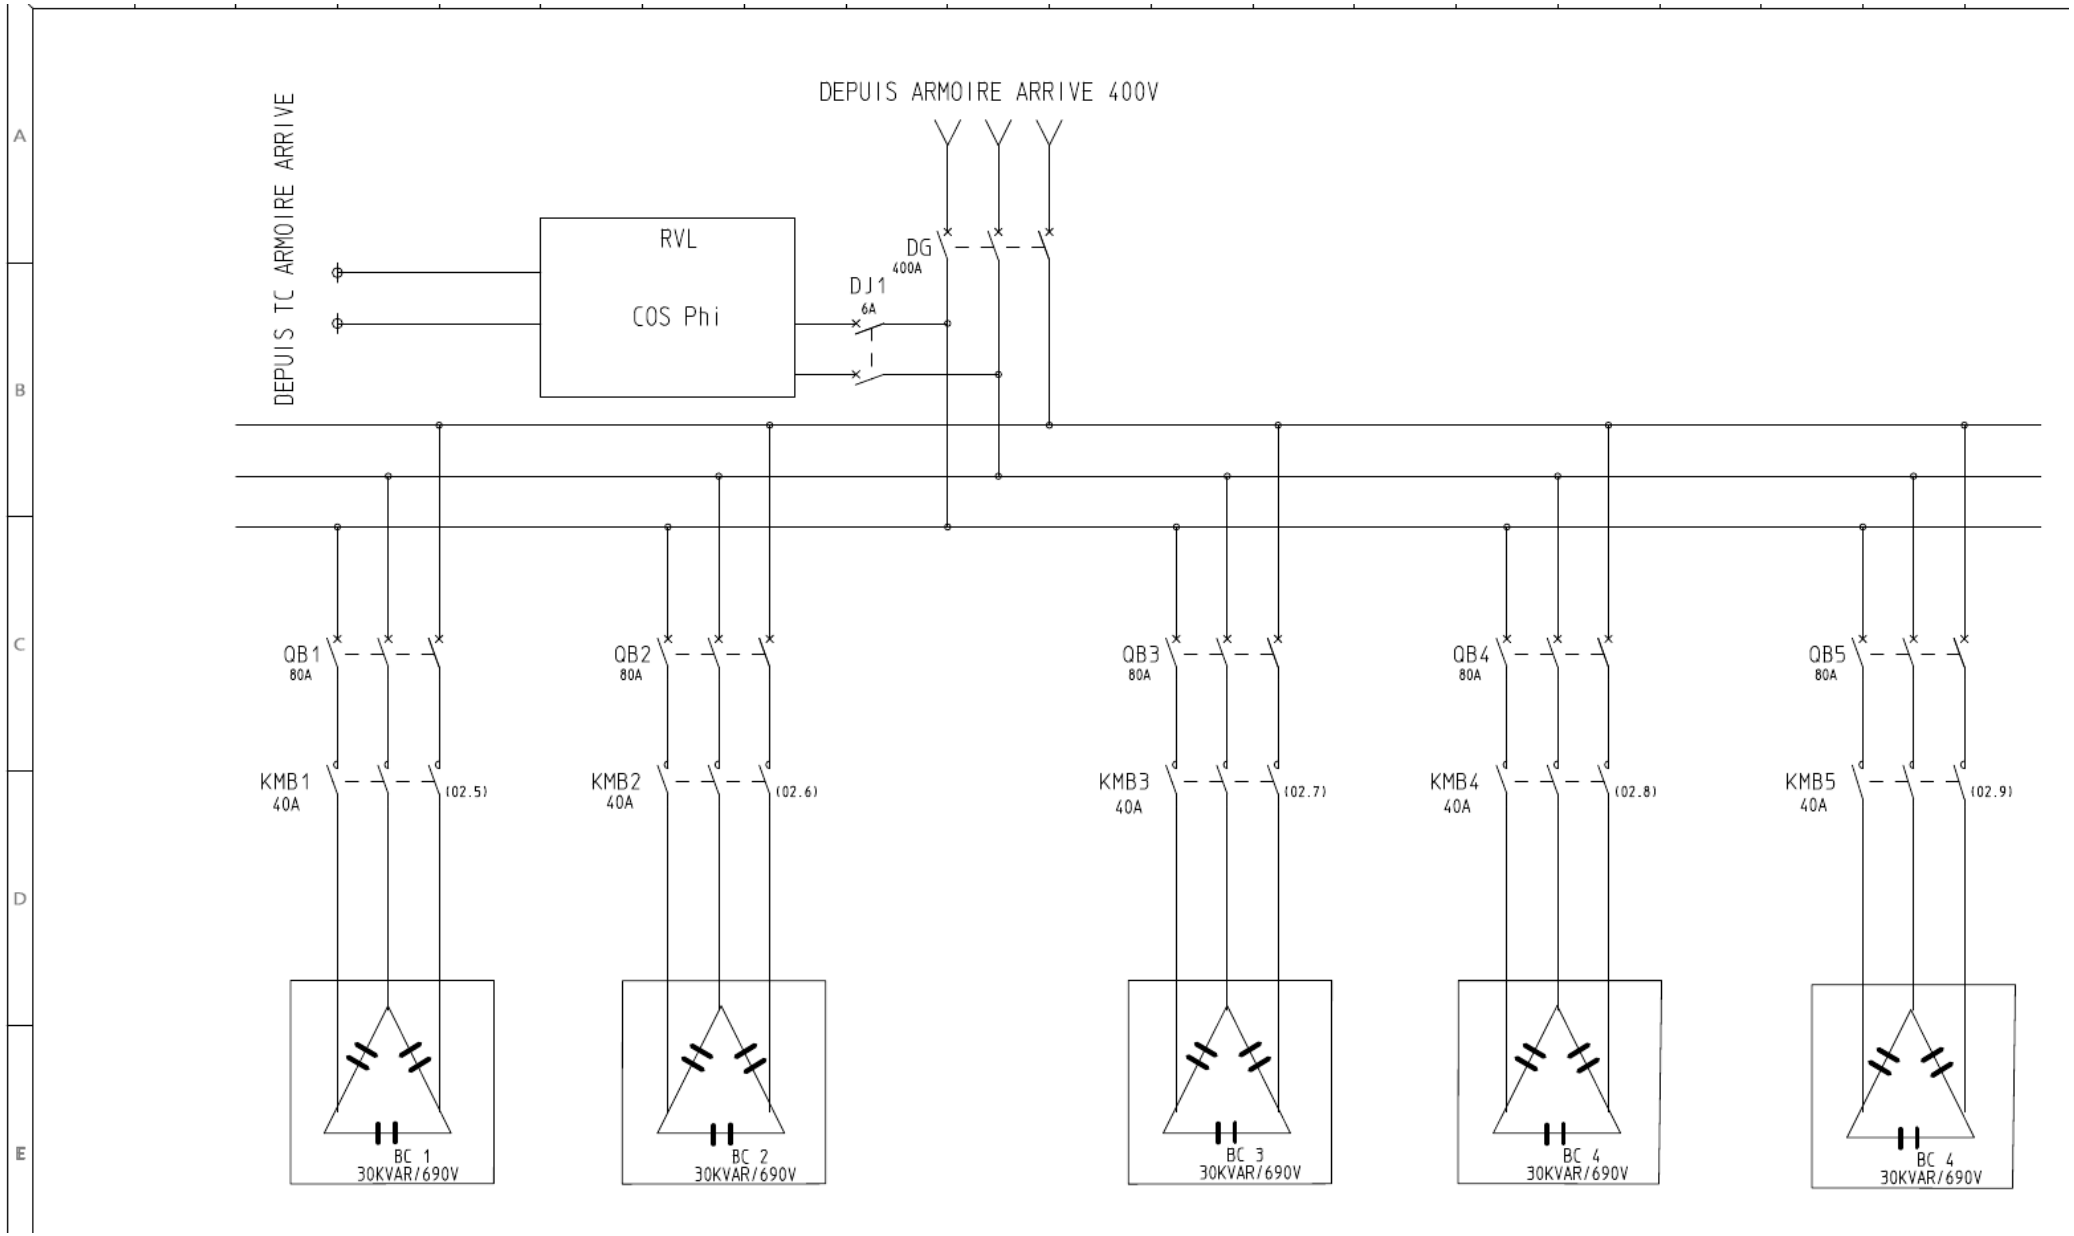


Normal / standby supply

Source-changeover and metering excerpt.

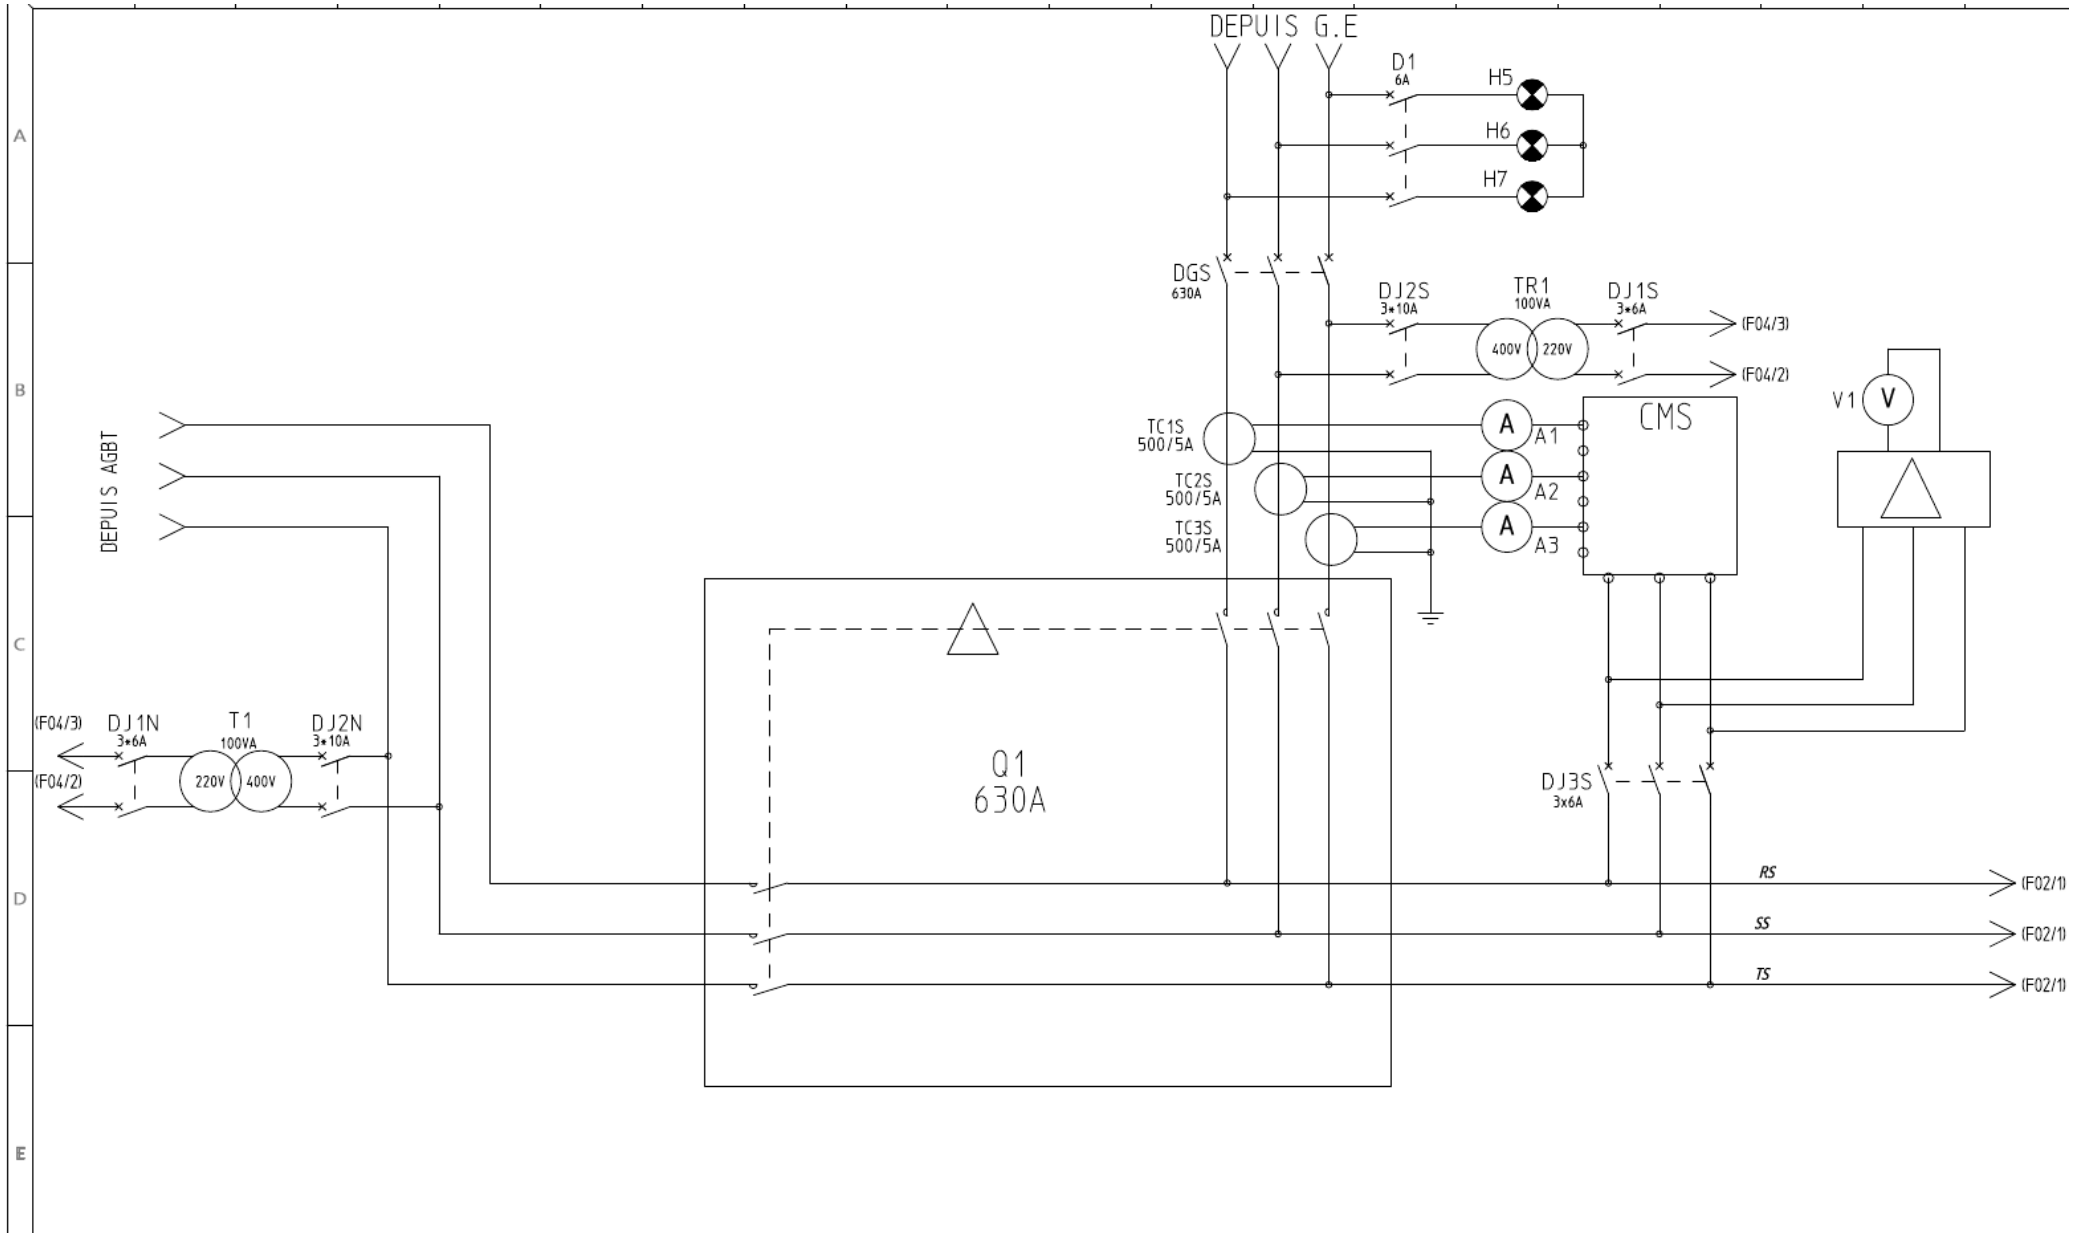


Blower motor control

Variable-speed drive and motor-control wiring.

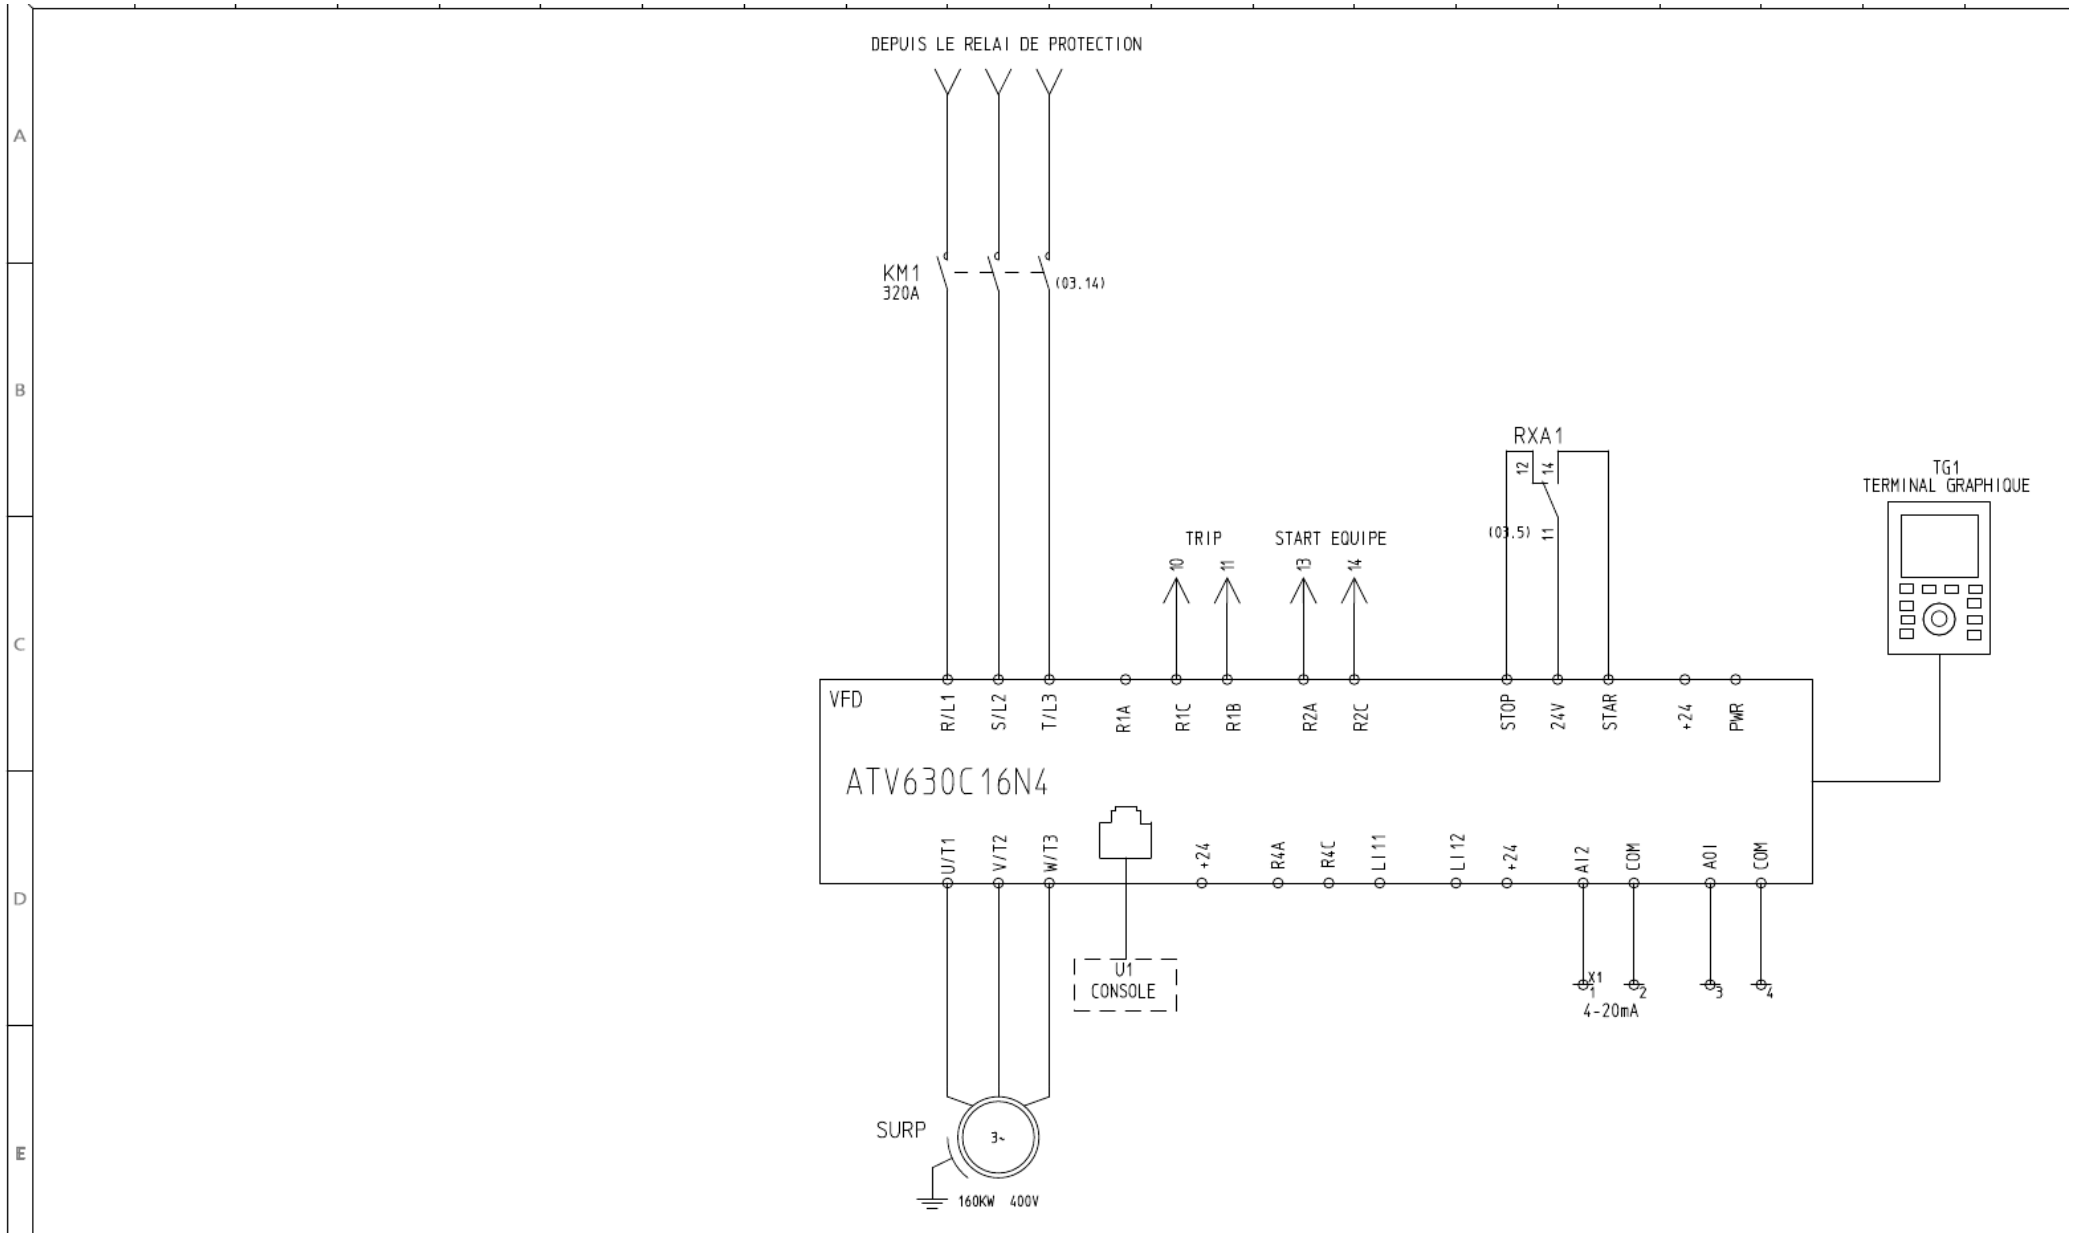

PLC input wiring


Digital input-card wiring and signal allocation.

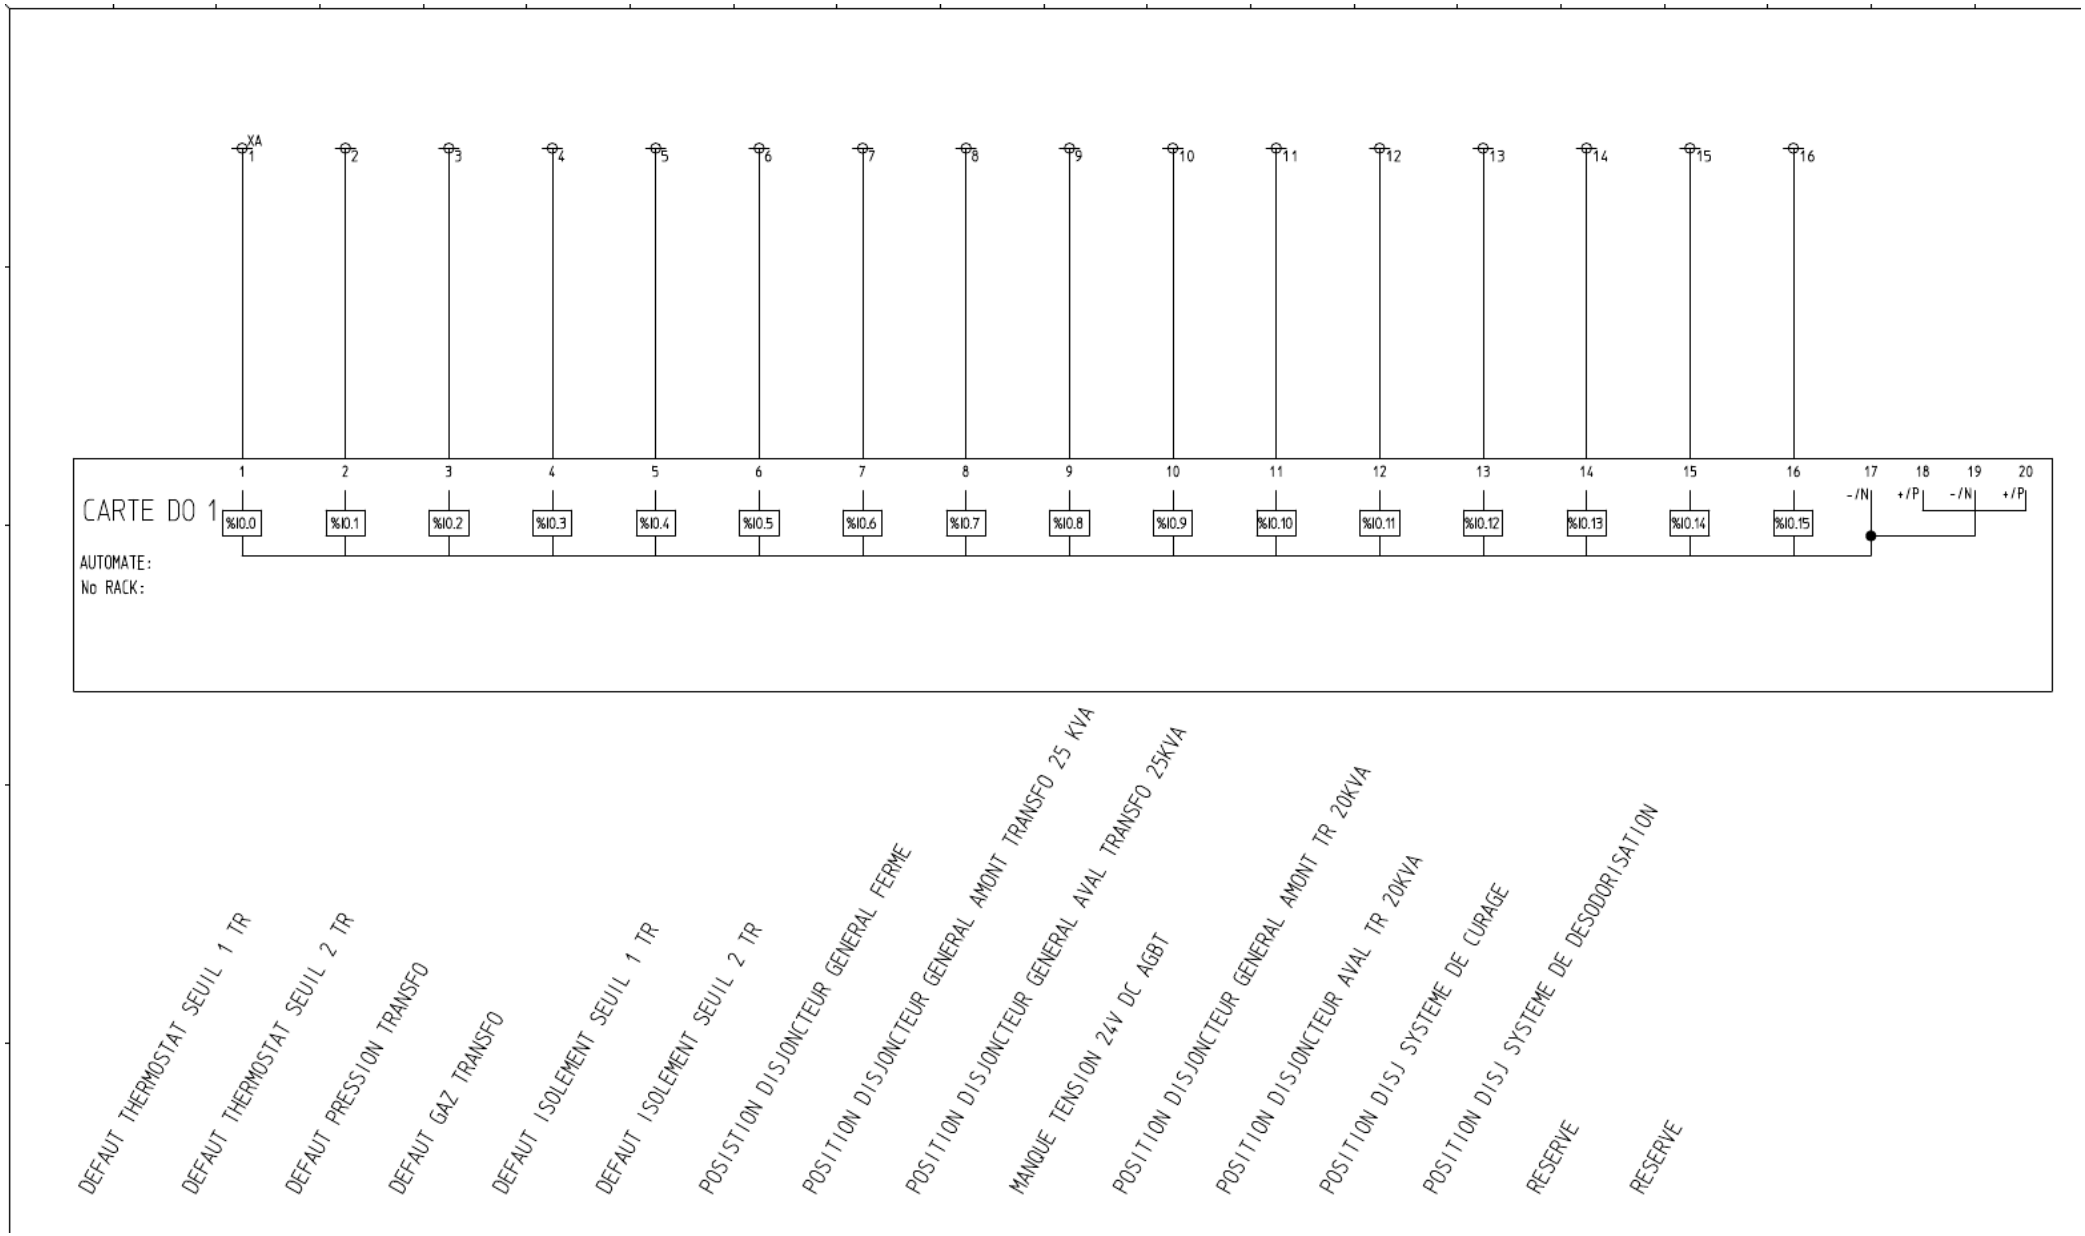

Selected team-project drawing. Portfolio excerpt; client title block excluded.


Pump protection circuit

Selected motor-protection and control-circuit excerpt.

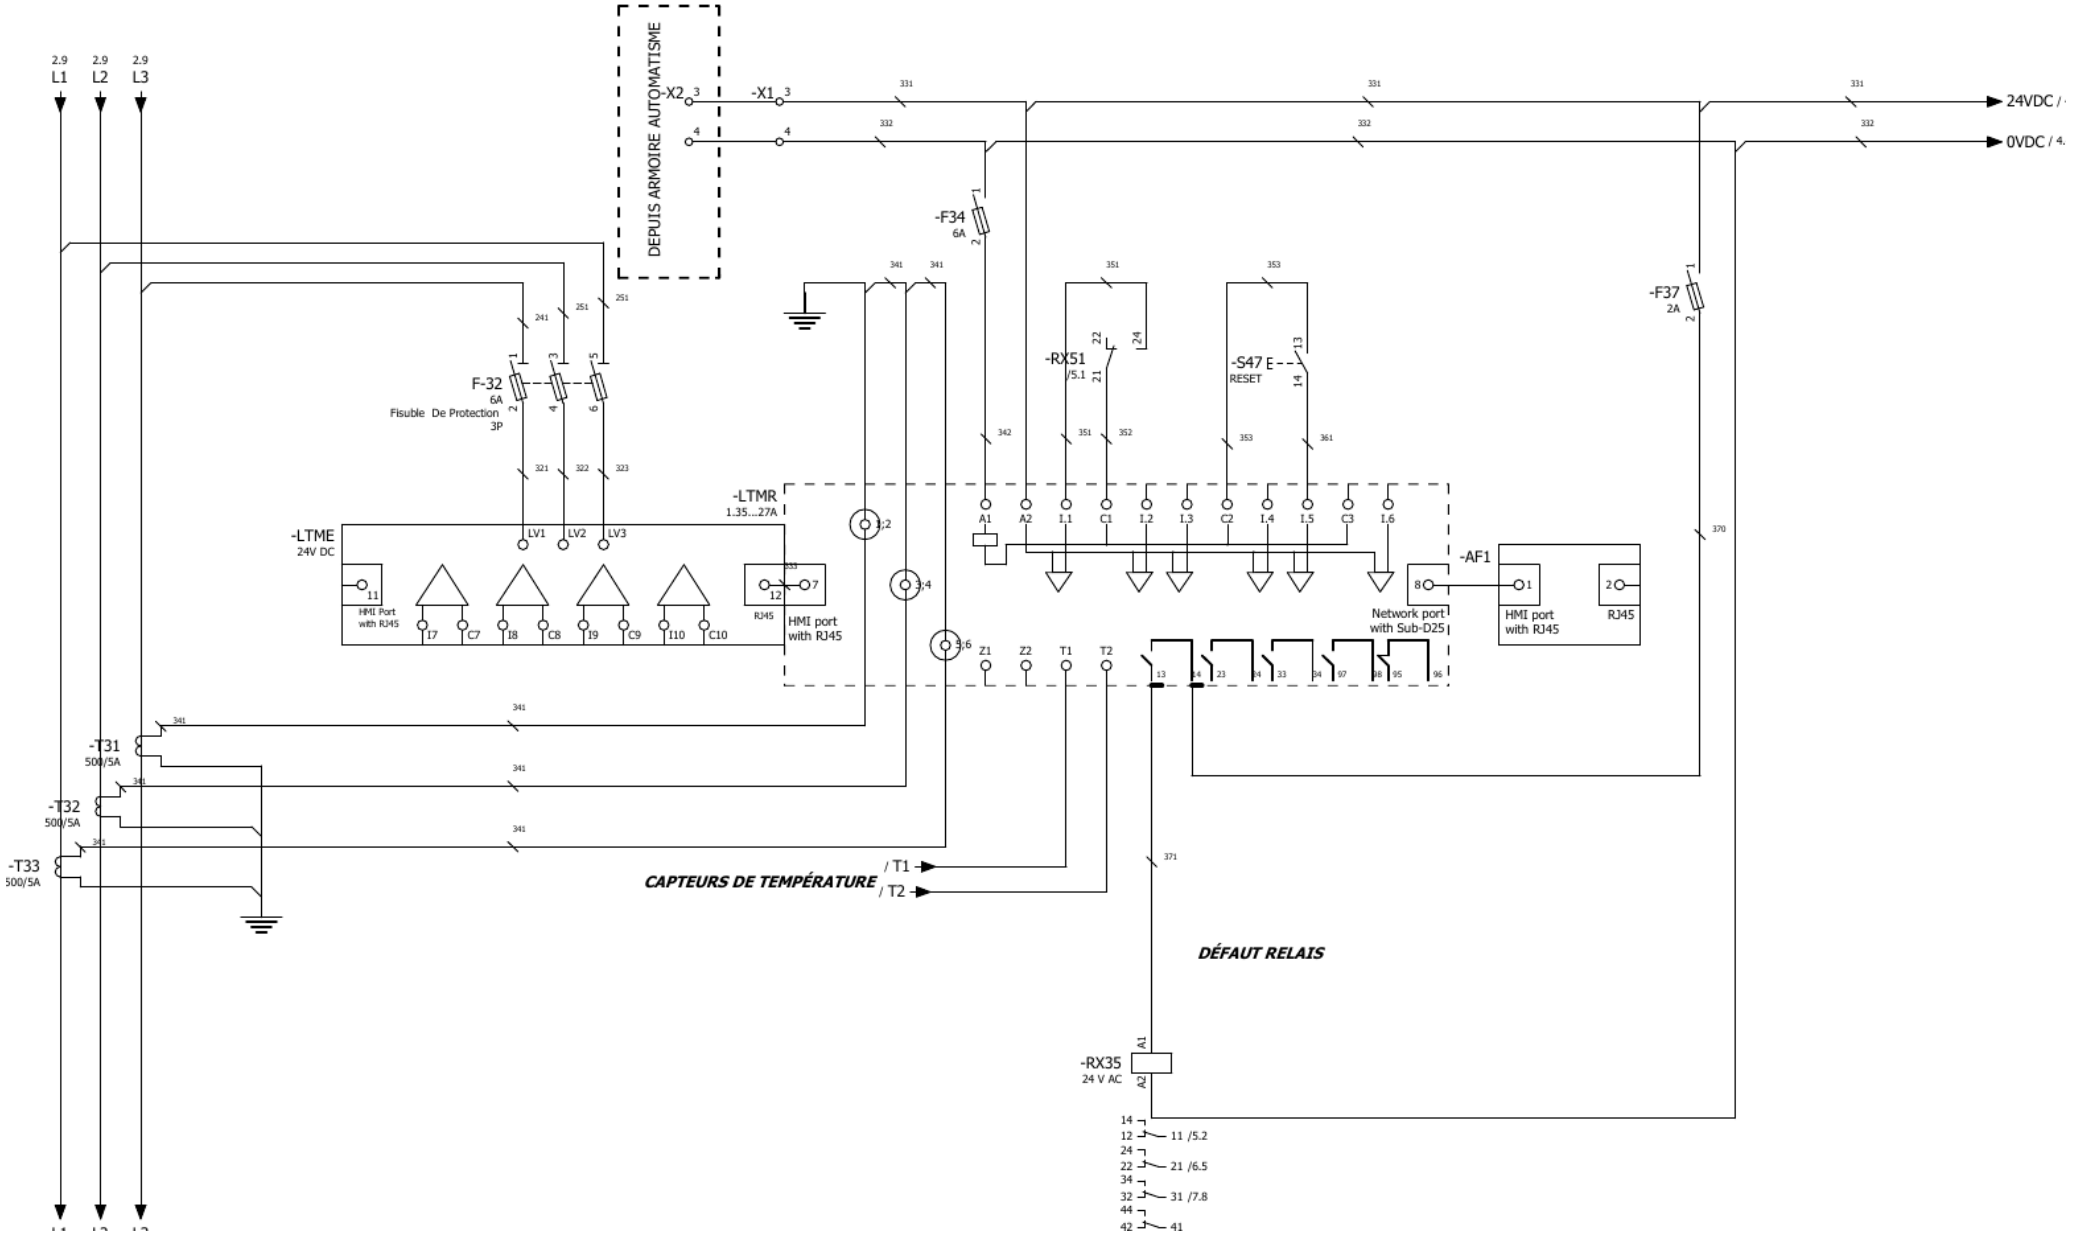

Automation I/O interconnection


Inter-panel analogue-signal connections.

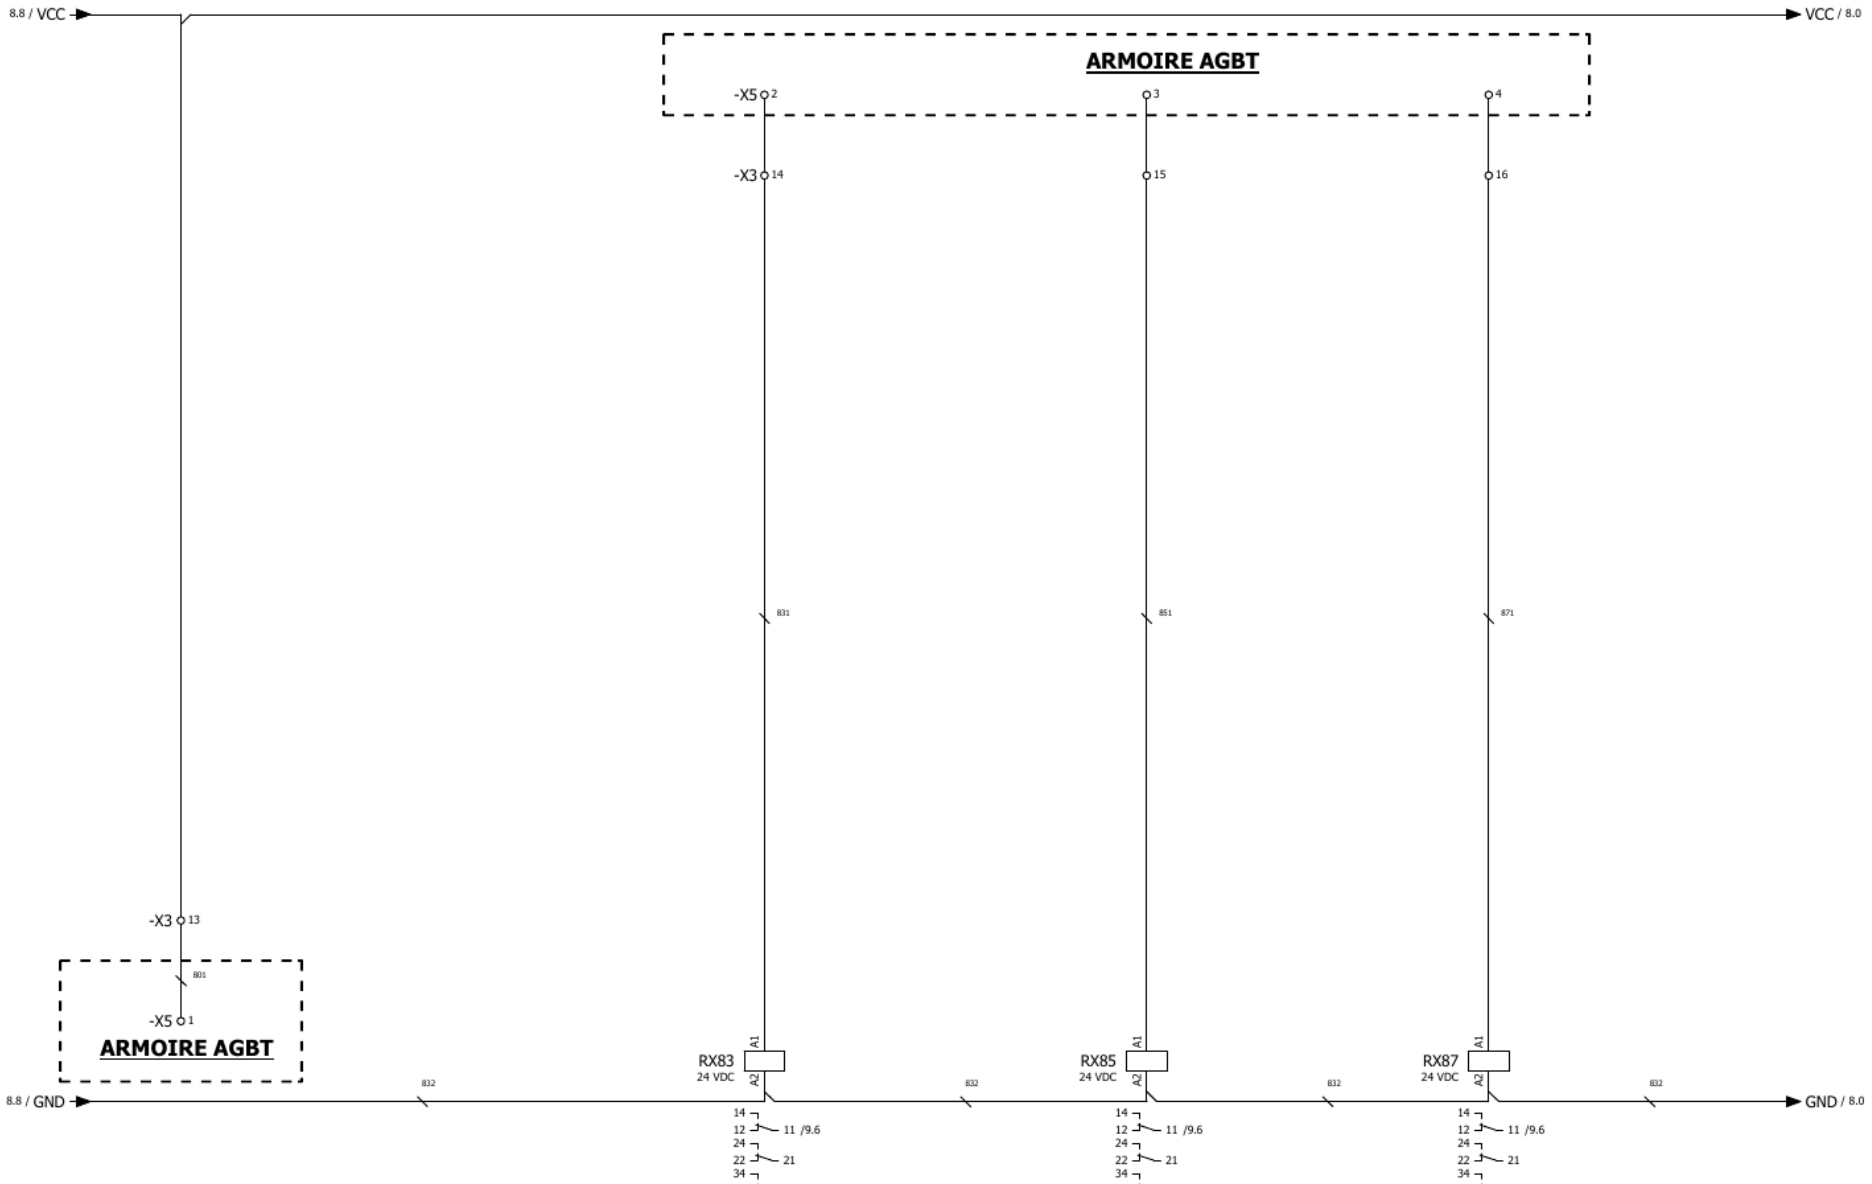

Selected team-project drawing. Portfolio excerpt; client title block excluded.

DGPT2 protection circuit

Transformer-protection signalling circuit.

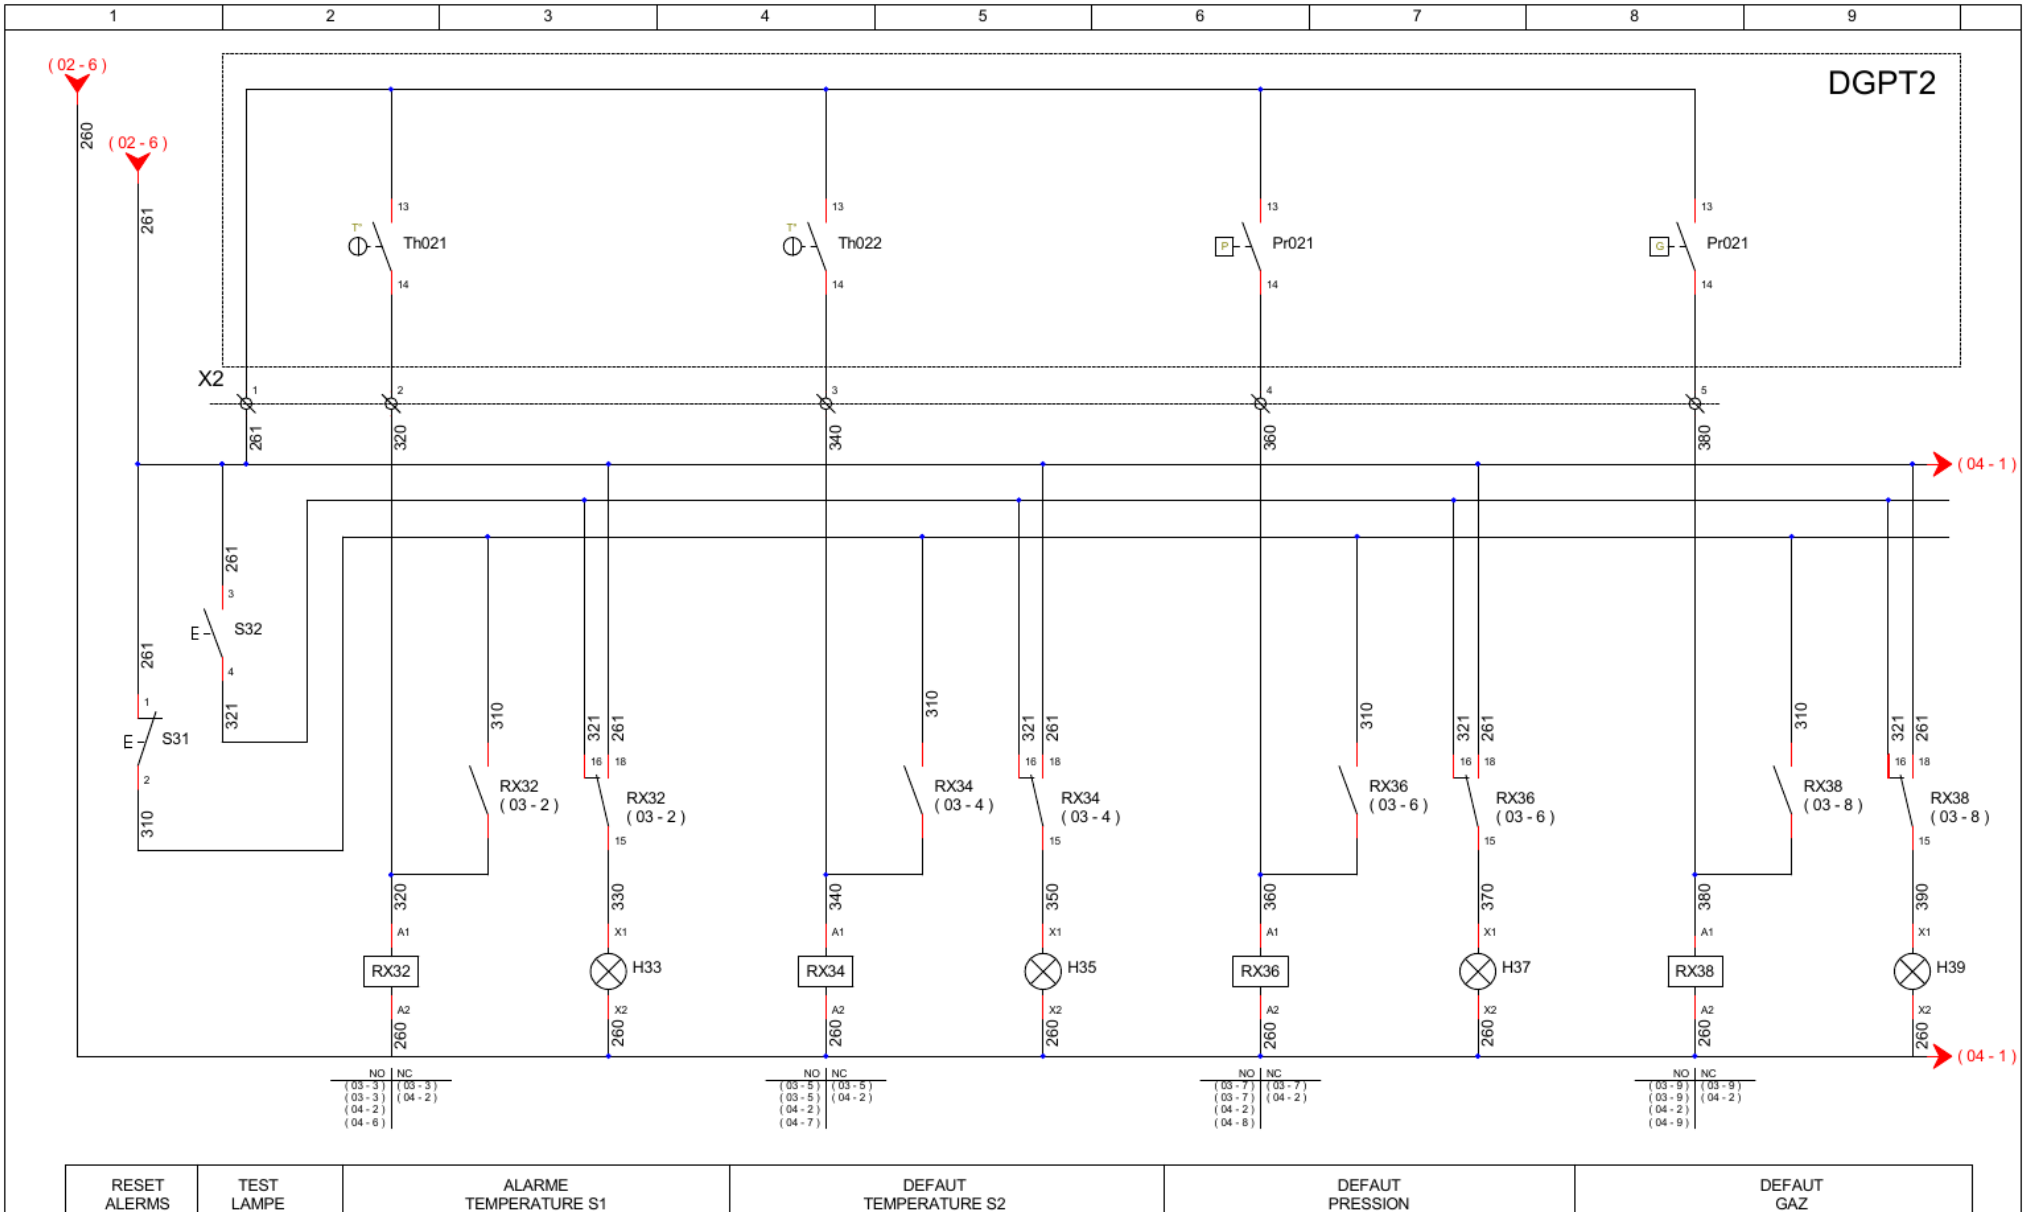

Electrical installation layout

Selected plan, section and transformer-installation views.

