
Industrial electrical installation | LV switchboard

Metering, current transformers and differential protection circuit.

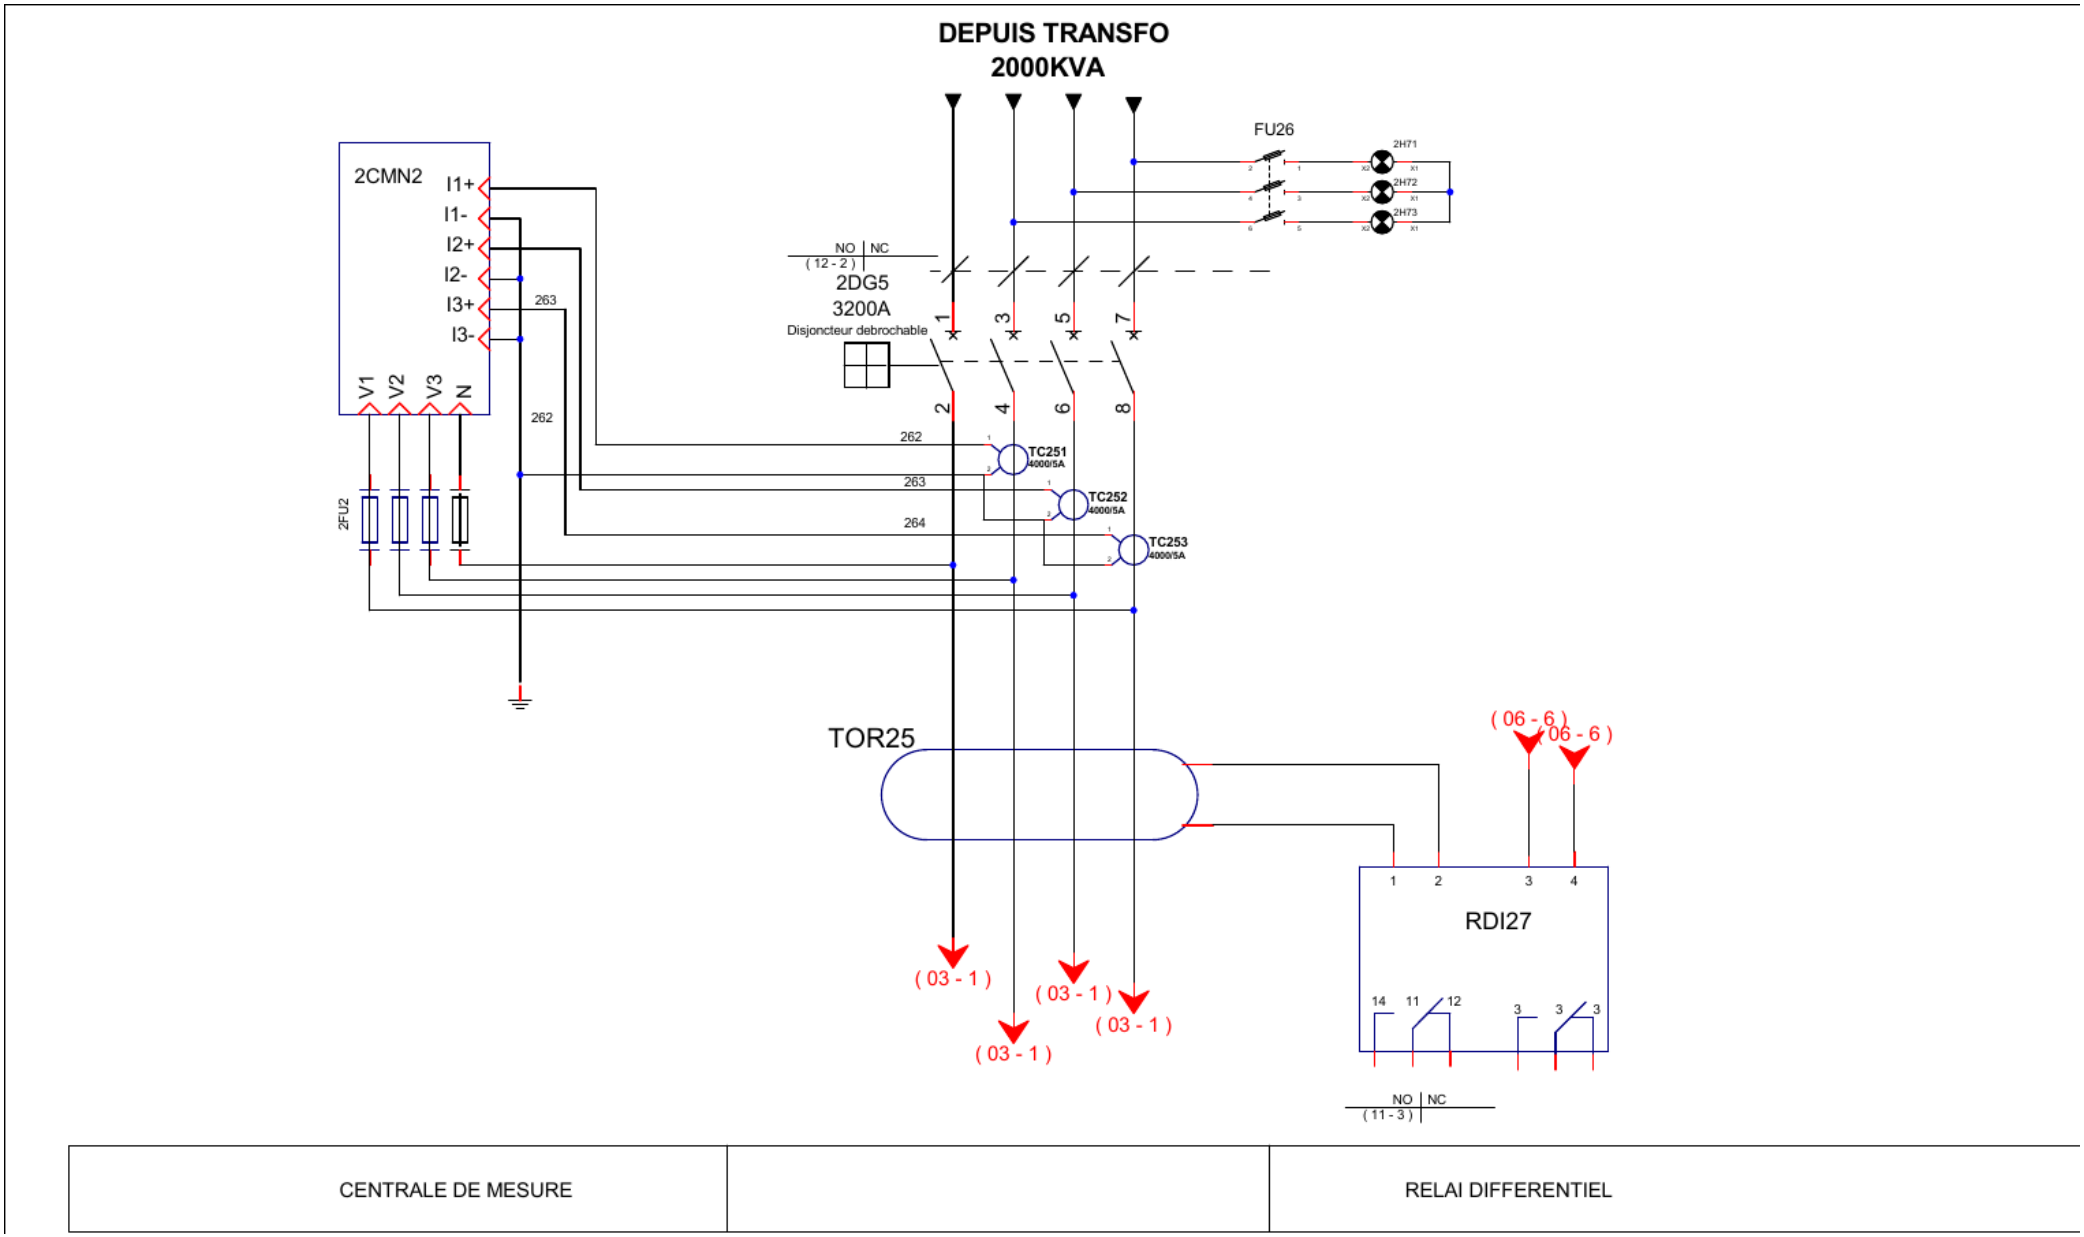

Selected team-project documentation. Personal contribution: studies, drawings, tests and commissioning.

Portfolio excerpt only. Client title block and contact information excluded.